



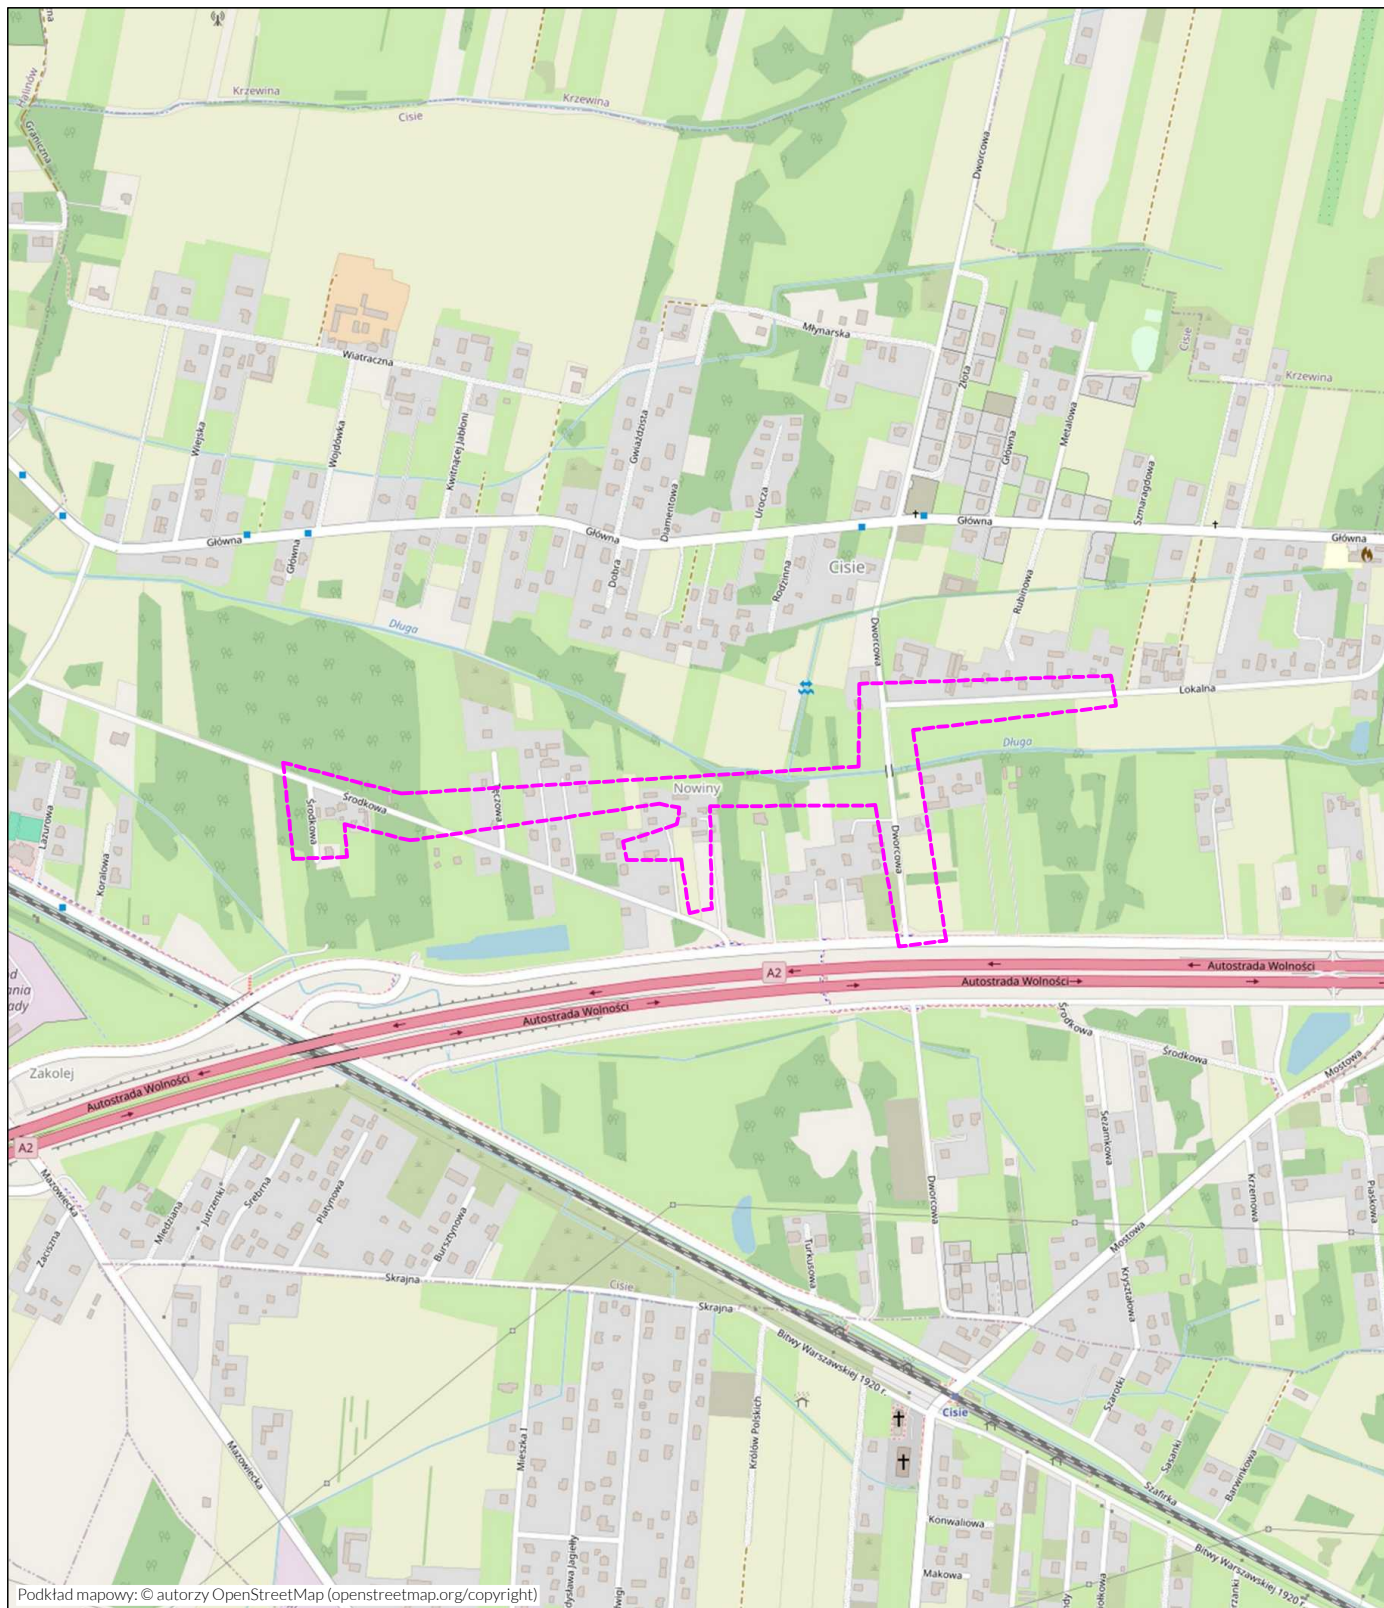


INWESTOR			
24IT Media sp. z o.o. ul. Wrzosowa 17 05-408 Glinianka			
Obiekt: Projektowane podwieszenie światłowodu na istn. słupach nN w miejscowości Cisie			
Stadium:		Numer stacji trafo:	Branża:
Projekt wykonawczy		03-0494	Telekomunikacja
Nr rysunku:	Skala:	Nazwa rysunku:	Data:
1	1:10 000	Plan orientacyjny	10.2026
Opracował:		Specjalność:	Nr uprawnień:
Projektant: inż. Tomasz Waśko		telekomunikacja	PDL/0137/PWOT/16
Projektant: mgr inż. Katarzyna Bukłaho		energetyka	PDL/0095/PWBE/22
Podpis:			

Sposób wprowadzenia światłowodu na słup nN typu żelbetowego

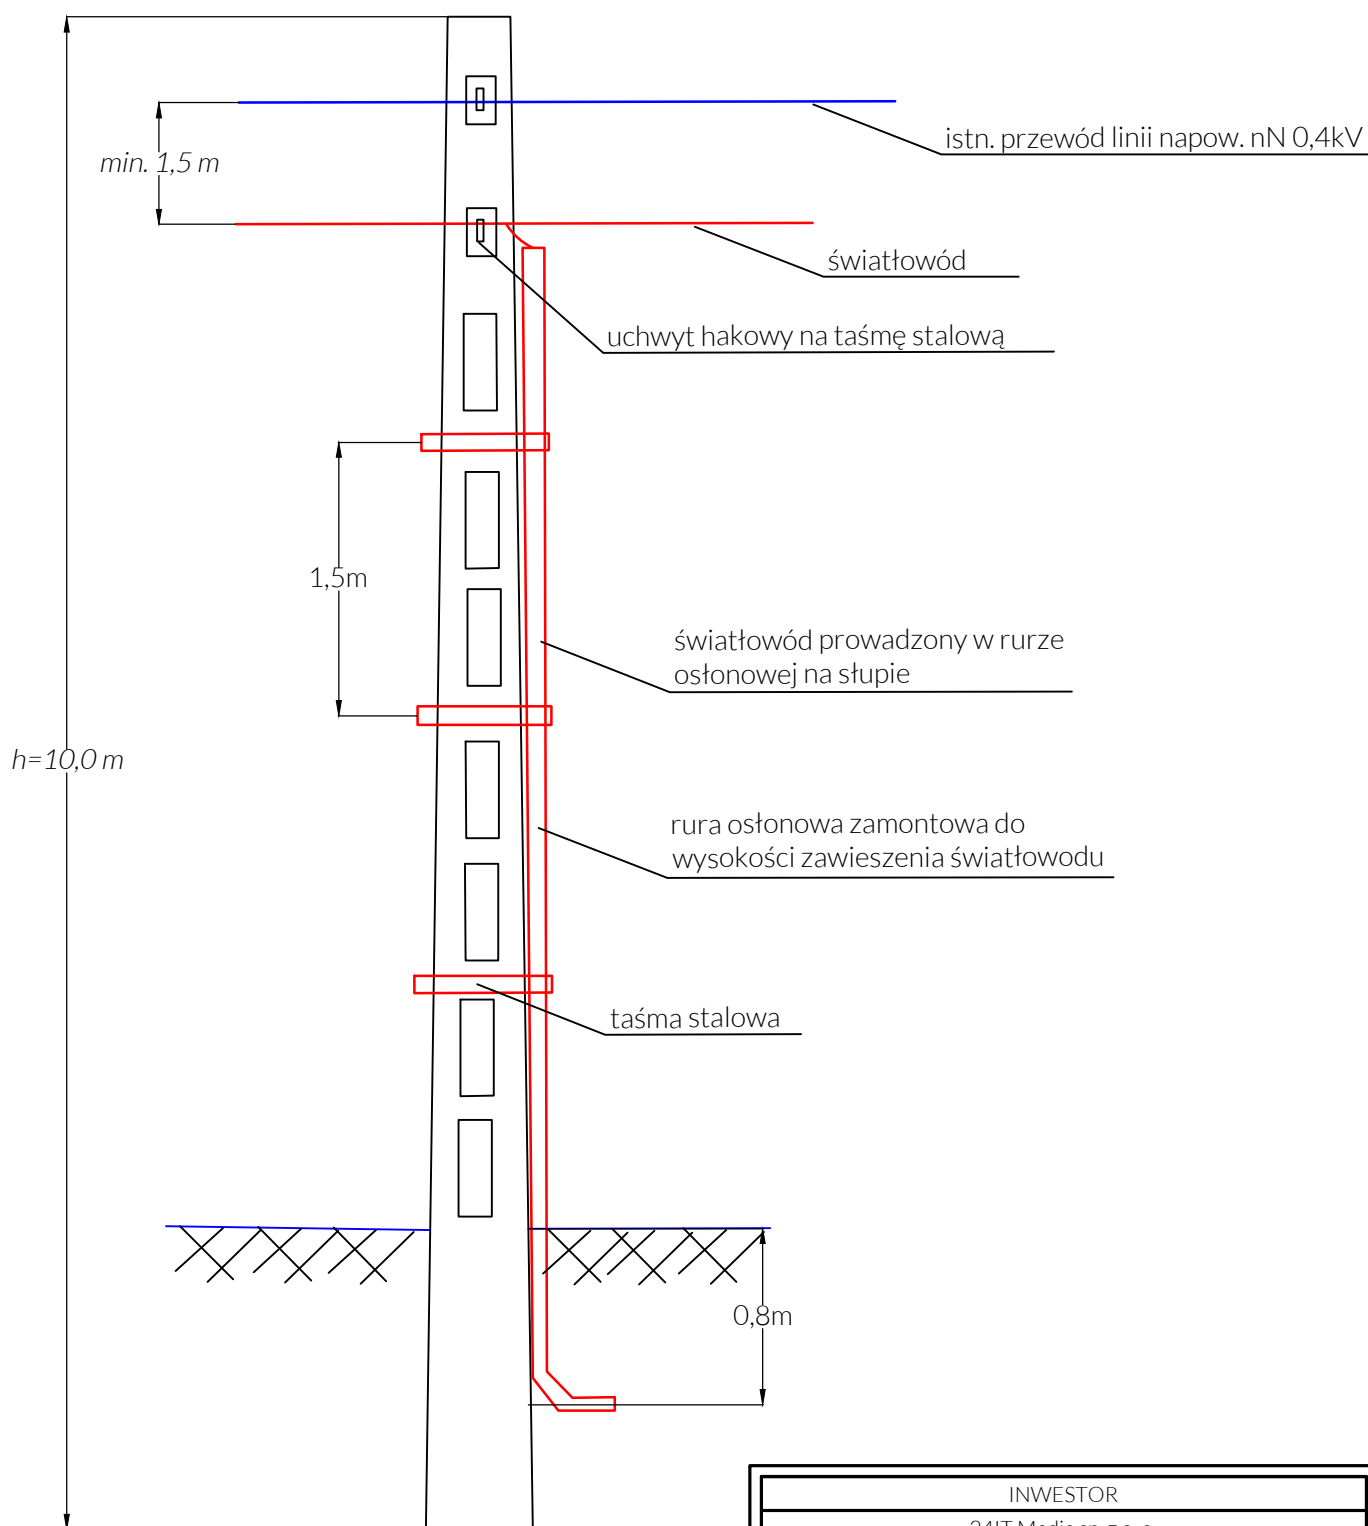


INWESTOR			
24IT Media sp. z o. o. ul. Wrzosowa 17 05-408 Glinianka			
Obiekt: Projektowane podwieszenie światłowodu na istn. słupach nN w miejscowości Cisie			
Stadium:		Numer stacji trafo:	Branża:
Projekt wykonawczy		03-0494	Telekomunikacja
Nr rysunku:	Skala:	Nazwa rysunku:	Data:
3.1	1:50	Widok zamontowania światłowodu - 1	10.2026
Opracował:	Specjalność:	Nr uprawnień:	Podpis:
Projektant: inż. Tomasz Waško	telekomunikacja	PDL/0137/PWOT/16	
Projektant: mgr inż. Katarzyna Bukłaho	energetyka	PDL/0095/PWBE/22	

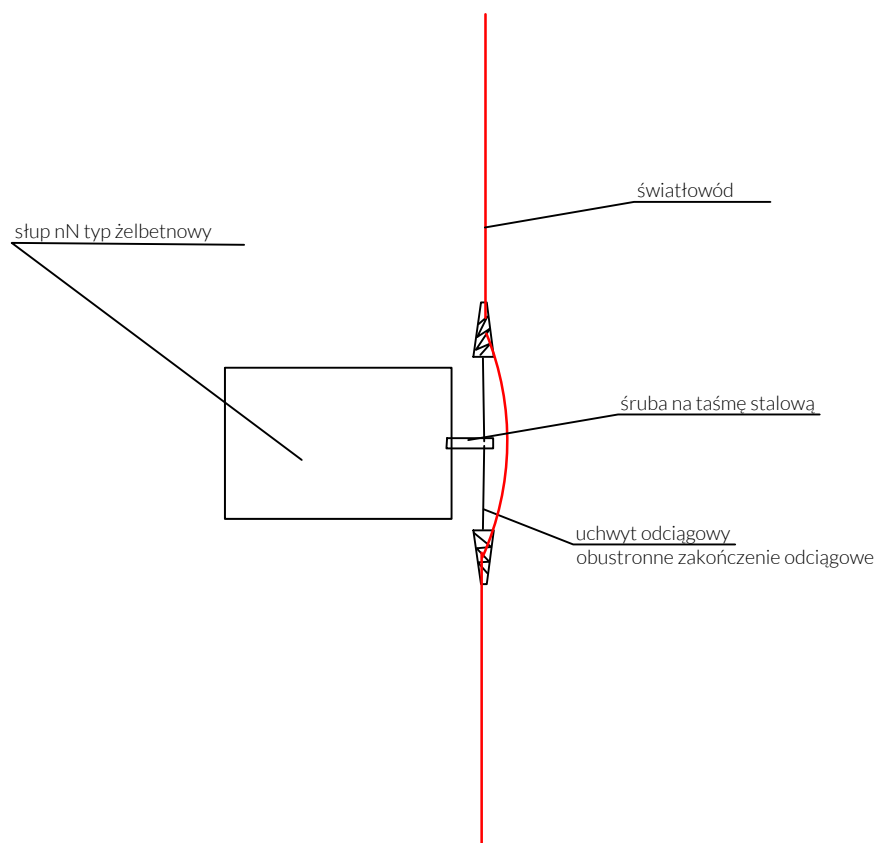


INWESTOR			
24IT Media sp. z o. o. ul. Wrzosowa 17 05-408 Glinianka			
Obiekt: Projektowane podwieszenie światłowodu na istn. słupach nN w miejscowości Cisie			
Stadium:		Numer stacji trafo:	Branża:
Projekt wykonawczy		03-0494	Telekomunikacja
Nr rysunku:	Skala:	Nazwa rysunku:	Data:
3.2	1:5	Widok zamontowania światłowodu - 2	10.2026
Opracował:	Specjalność:	Nr uprawnień:	Podpis:
Projektant: inż. Tomasz Waśko	telekomunikacja	PDL/0137/PWOT/16	
Projektant: mgr inż. Katarzyna Bukłaho	energetyka	PDL/0095/PWBE/22	

Sposób wprowadzenia światłowodu na
słup nN typu wirowanego

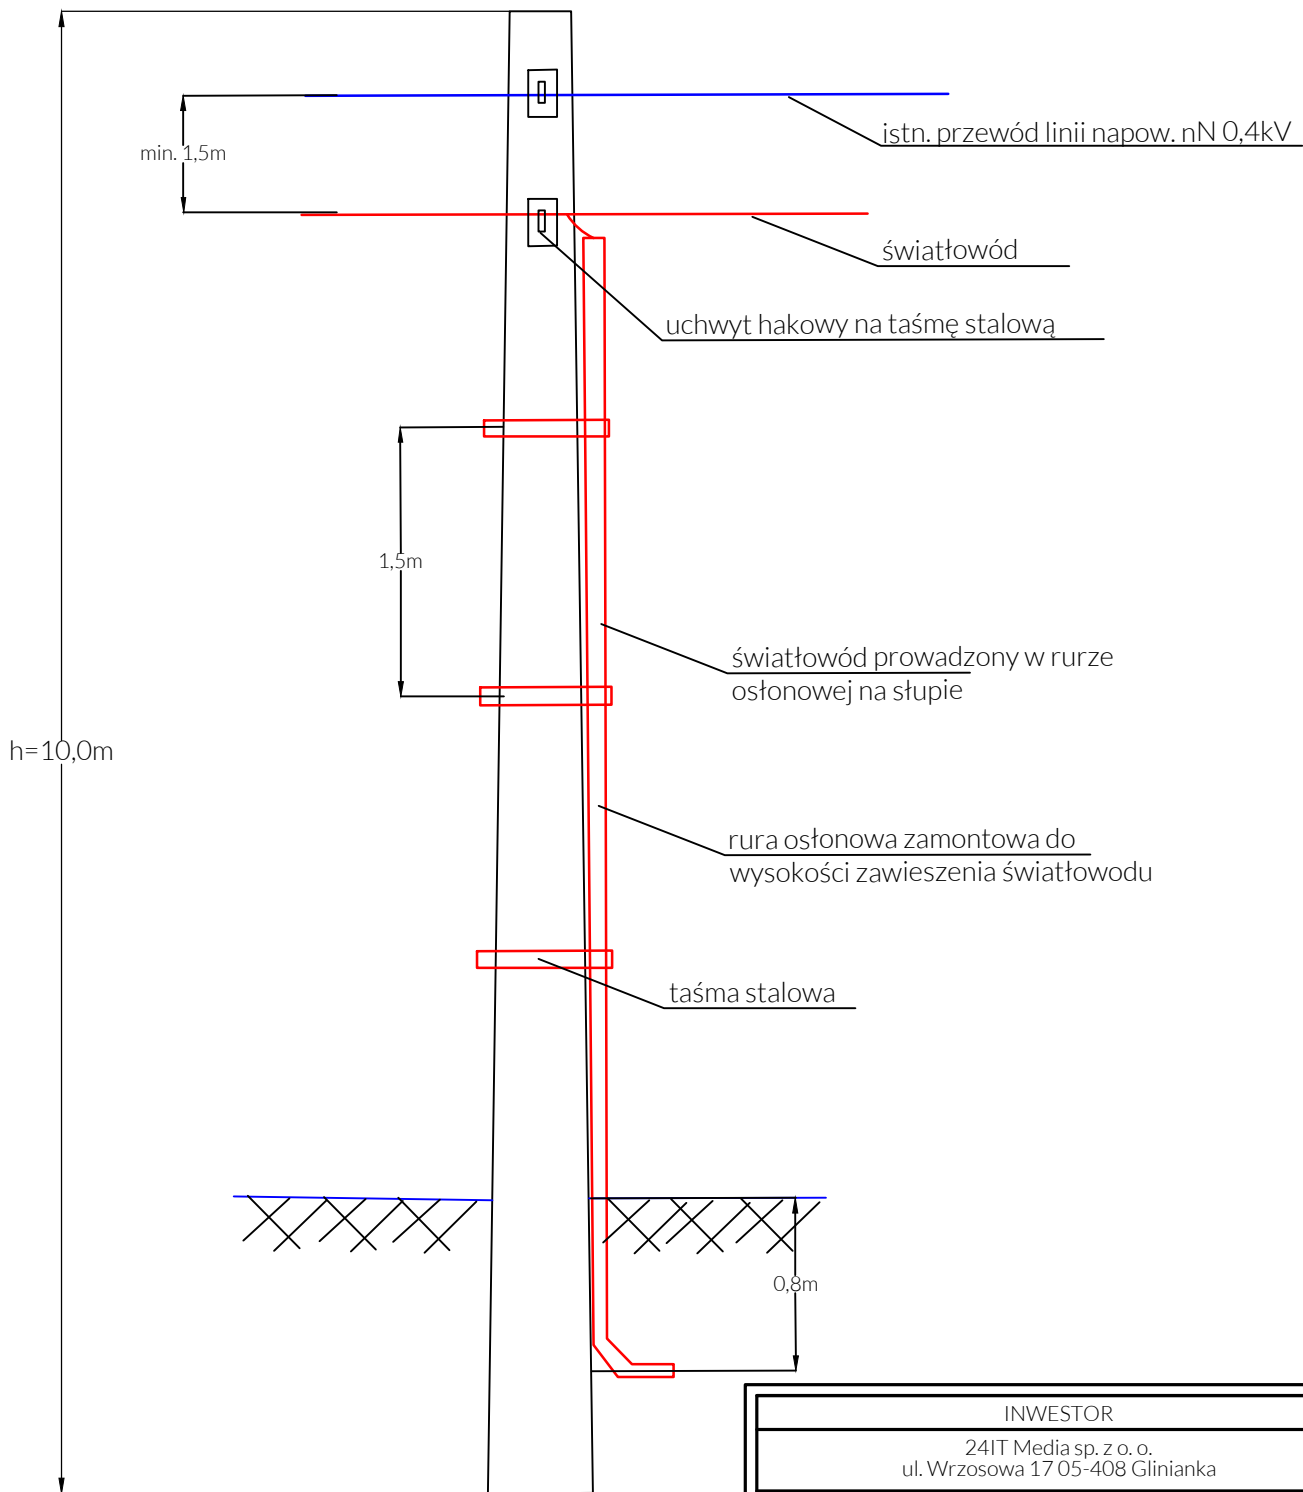

INWESTOR			
24IT Media sp. z o. o. ul. Wrzosowa 17 05-408 Glinianka			
Obiekt: Projektowane podwieszenie światłowodu na istn. słupach nN w miejscowości Cisie			
Stadium: Projekt wykonawczy		Numer stacji trafo: 03-0494	Branża: Telekomunikacja
Nr rysunku: 3.3	Skala: 1:50	Nazwa rysunku: Widok zamontowania światłowodu - 3	Data: 10.2026
Opracował: Specjalność: Nr uprawnień: Podpis:			
Projektant: inż. Tomasz Waśko		telekomunikacja	PDL/0137/PWOT/16
Projektant: mgr inż. Katarzyna Bukłaho		energetyka	PDL/0095/PWBE/22

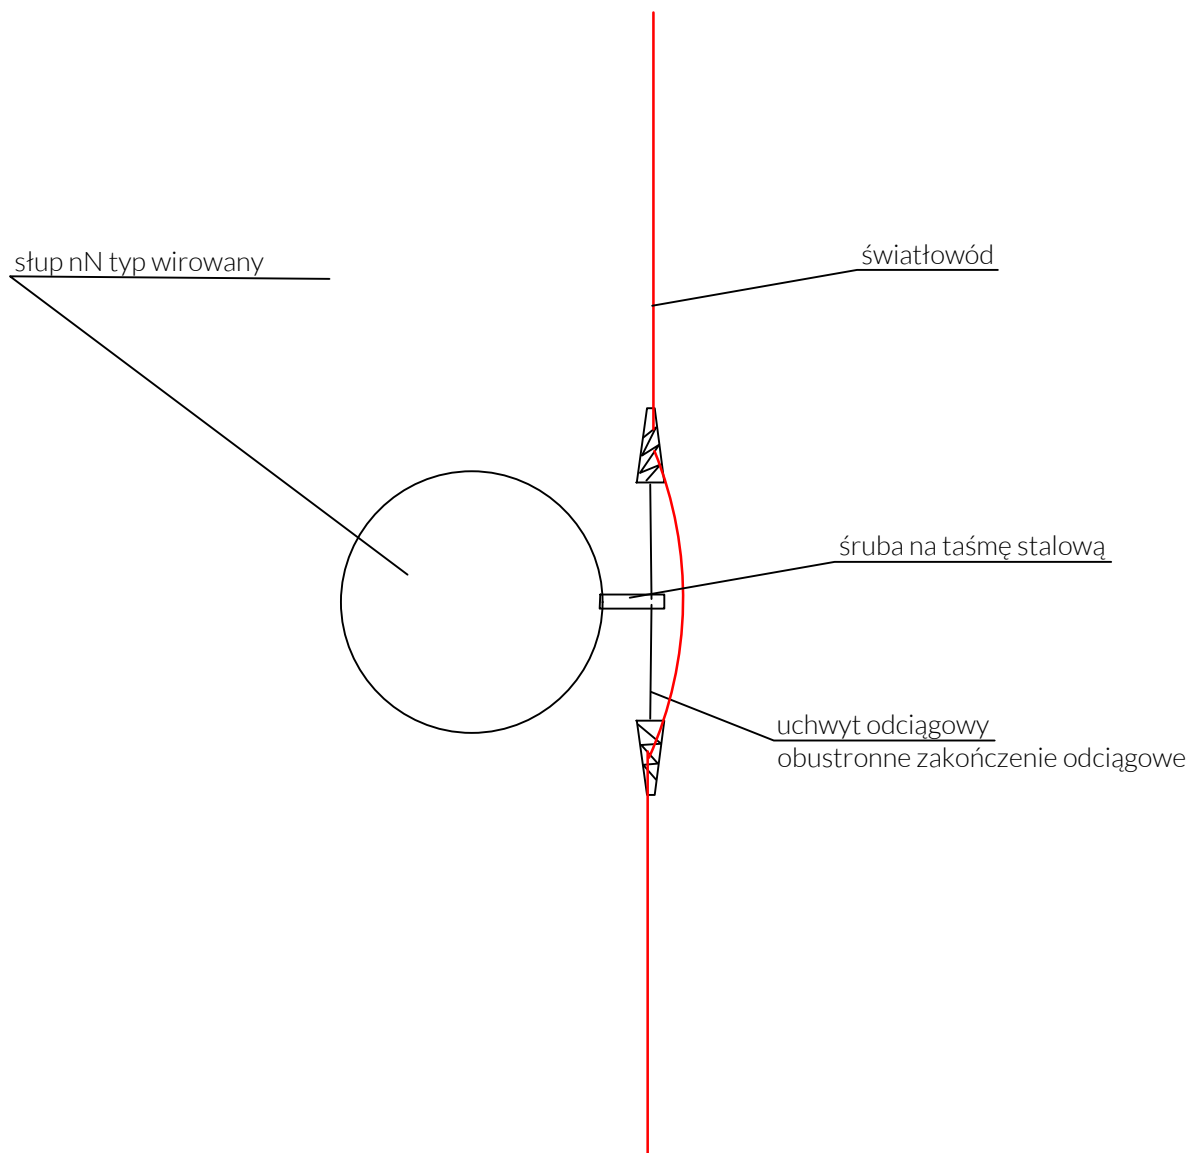

INWESTOR			
24IT Media sp. z o. o. ul. Wrzosowa 17 05-408 Glinianka			
Obiekt: Projektowane podwieszenie światłowodu na istn. słupach nN w miejscowości Cisie			
Stadium:		Numer stacji trafo:	Branża:
Projekt wykonawczy		03-0494	Telekomunikacja
Nr rysunku:	Skala:	Nazwa rysunku:	Data:
3.4	1:5	Widok zamontowania światłowodu - 4	10.2026
Opracował:	Specjalność:	Nr uprawnień:	Podpis:
Projektant: inż. Tomasz Waśko	telekomunikacja	PDL/0137/PWOT/16	
Projektant: mgr inż. Katarzyna Bukłaho	energetyka	PDL/0095/PWBE/22	